



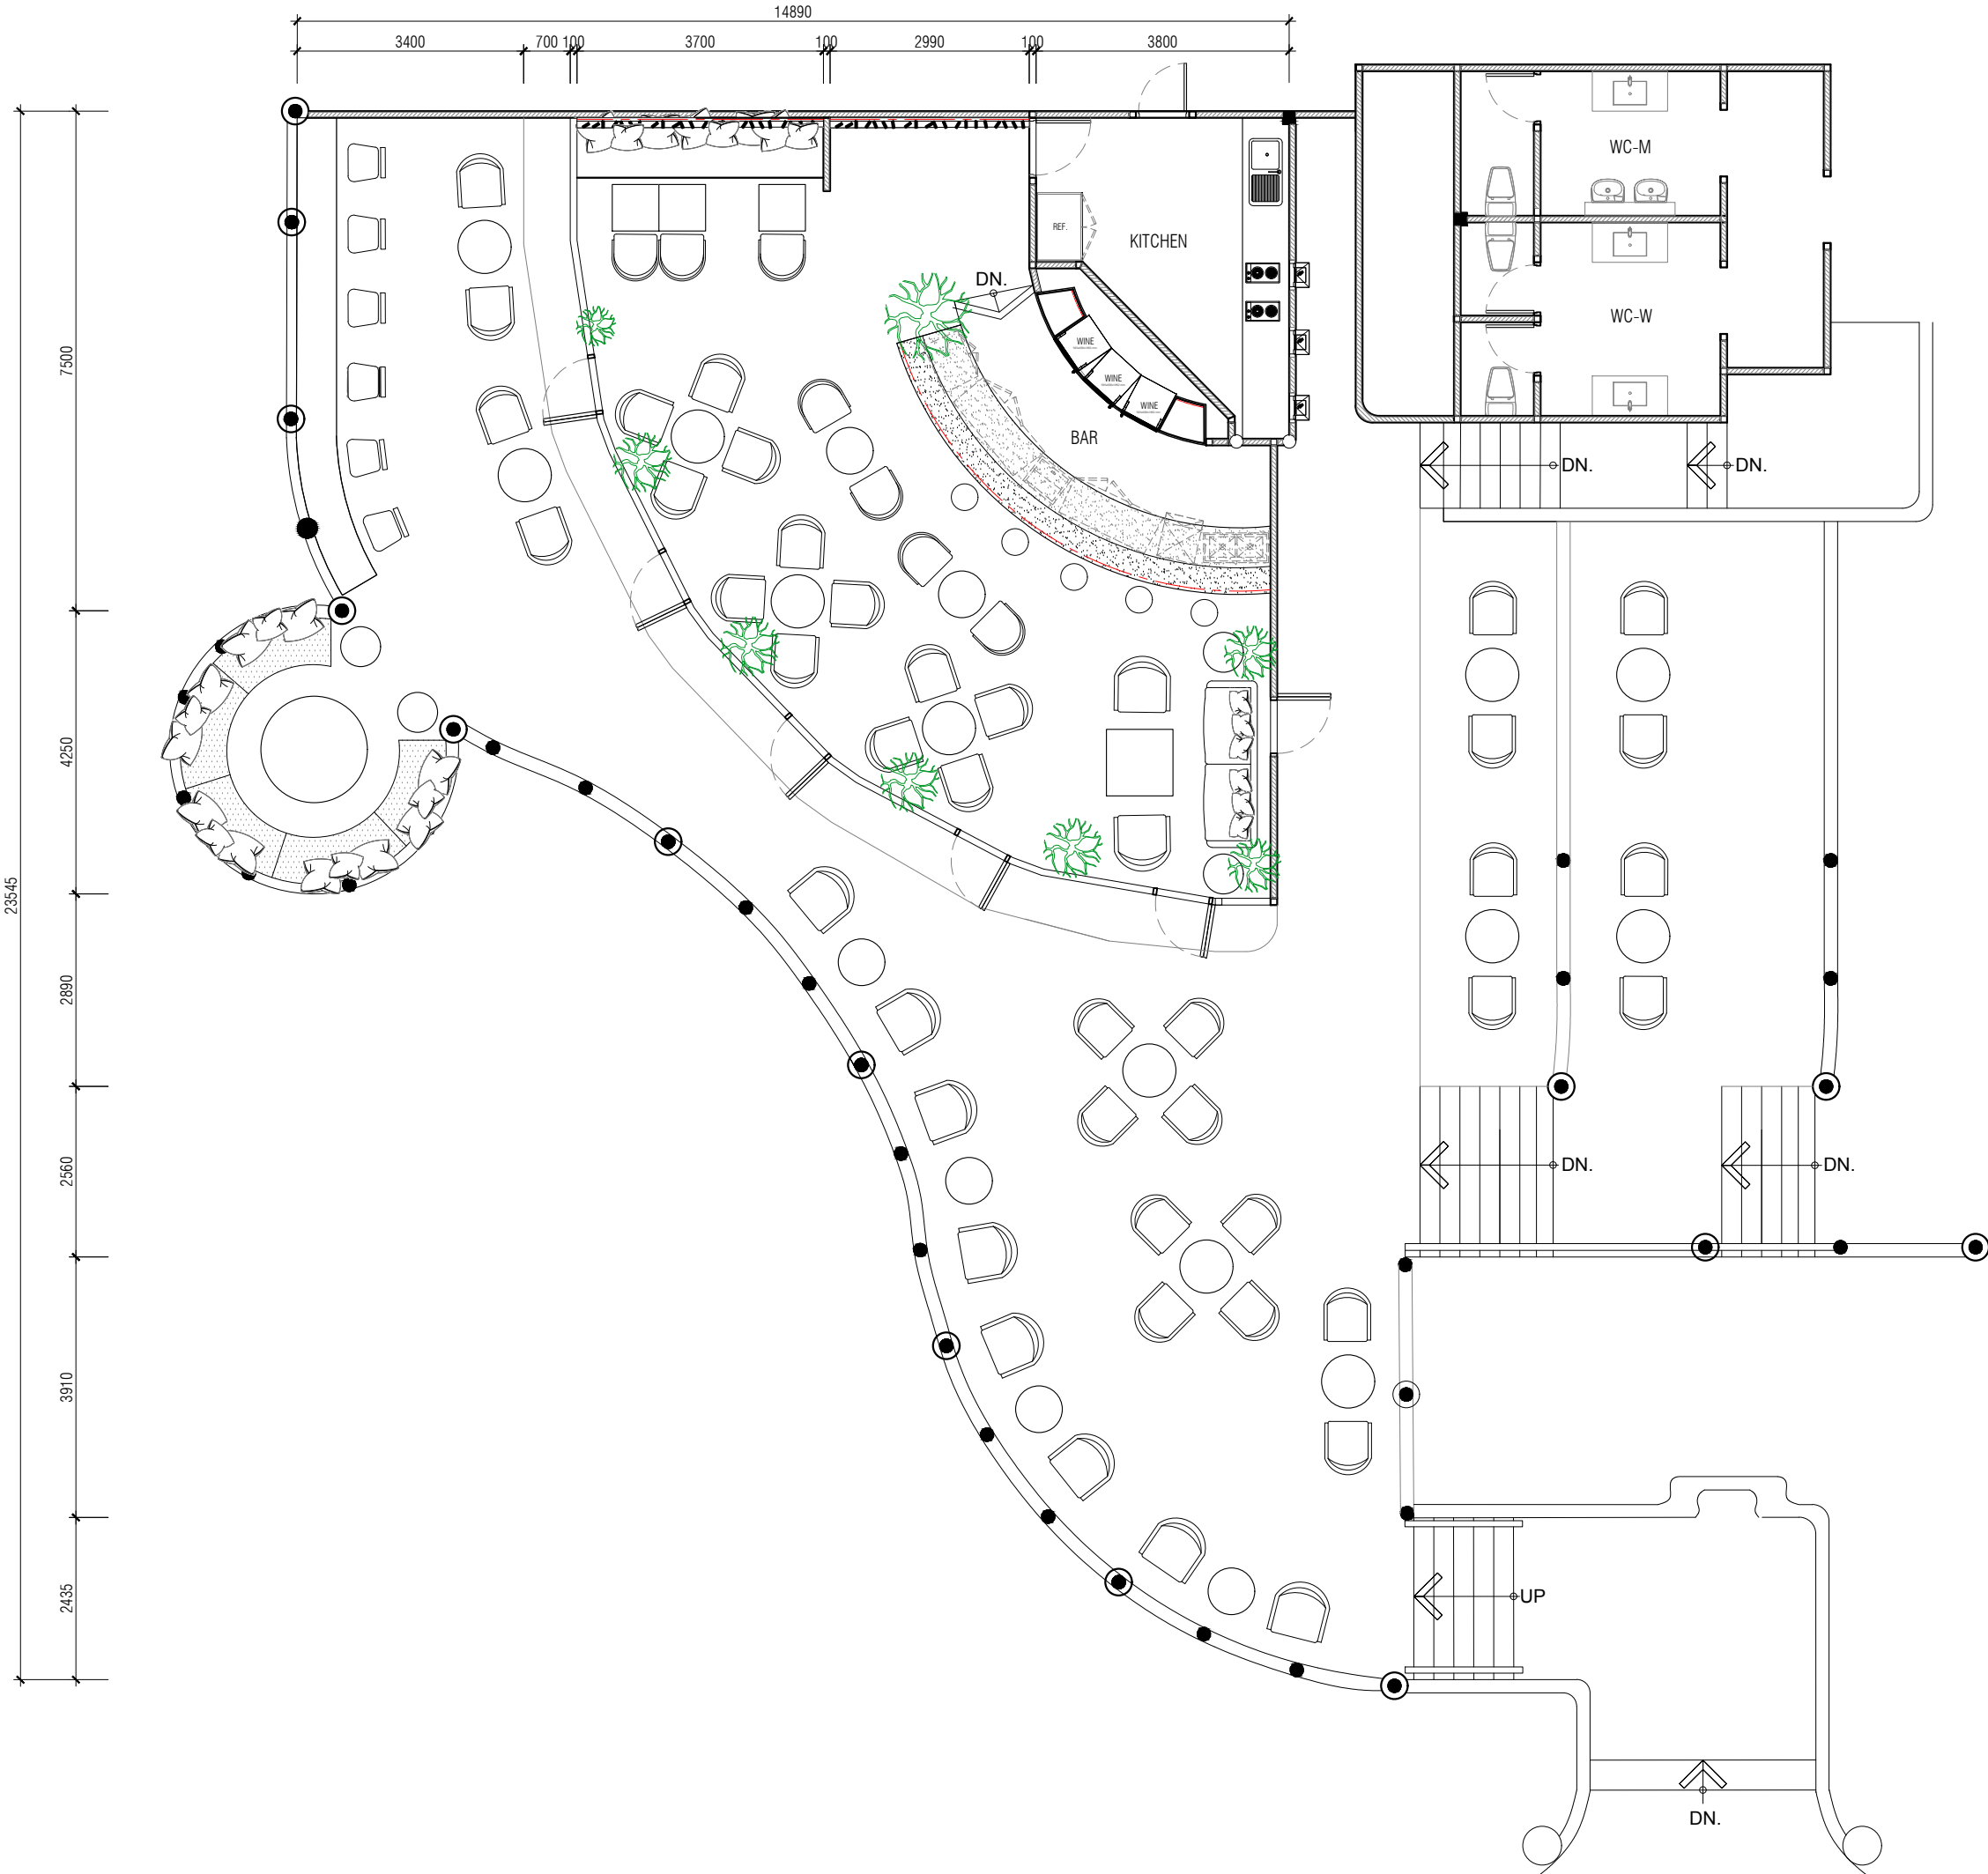


FURNITURE LAYOUT PLAN 1 : 100
SUNSETBAR

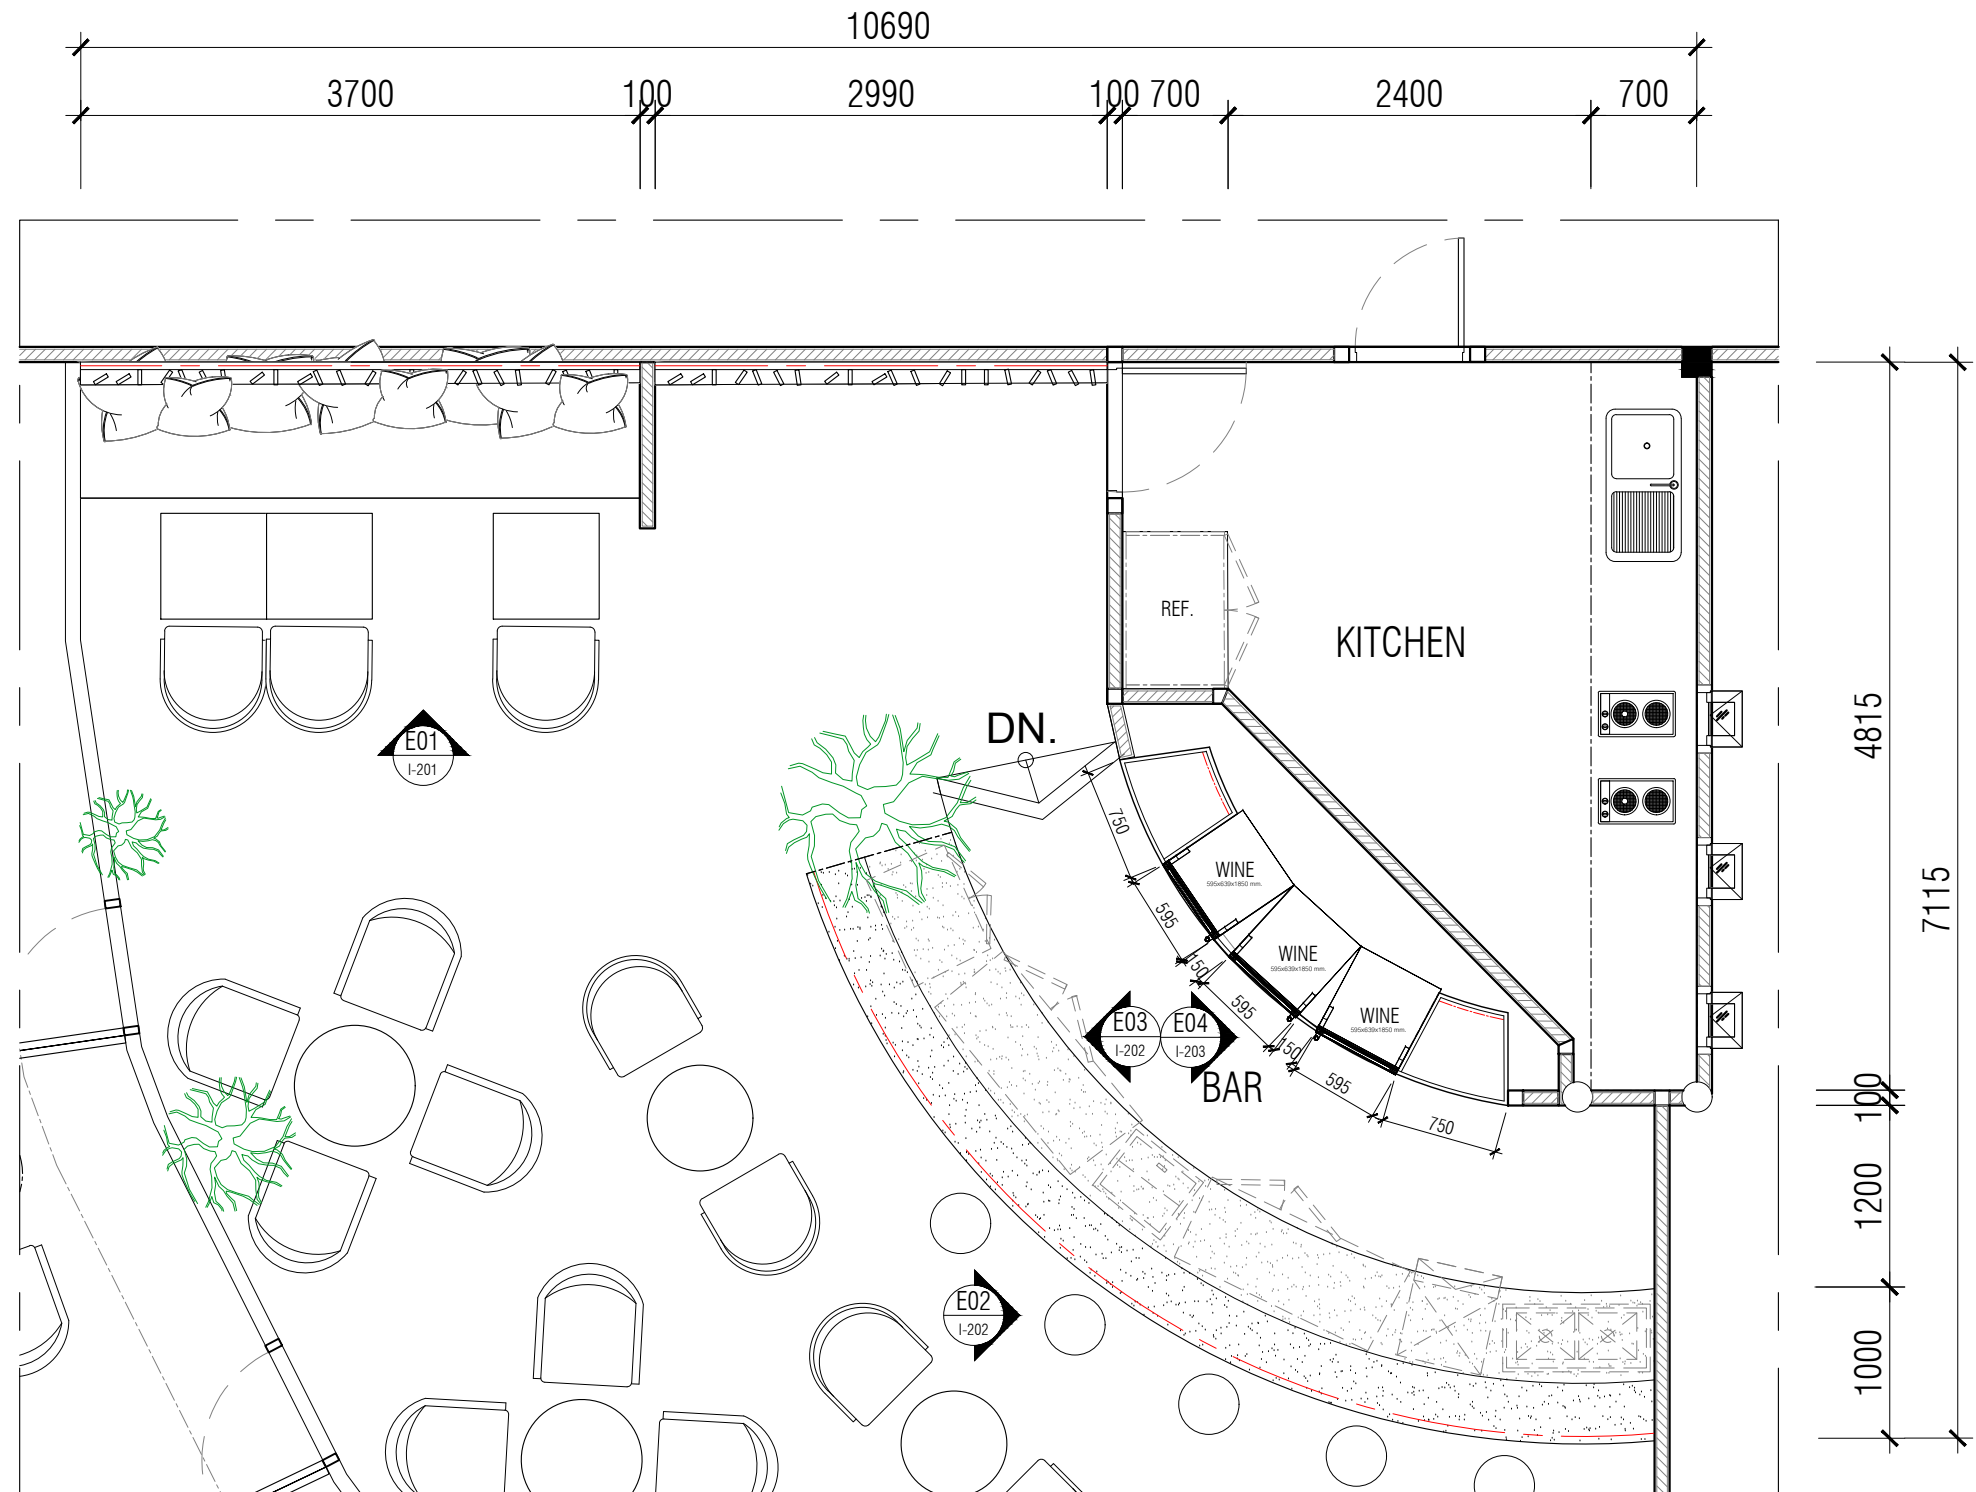


FURNITURE LAYOUT PLAN 1 : 50

BAR

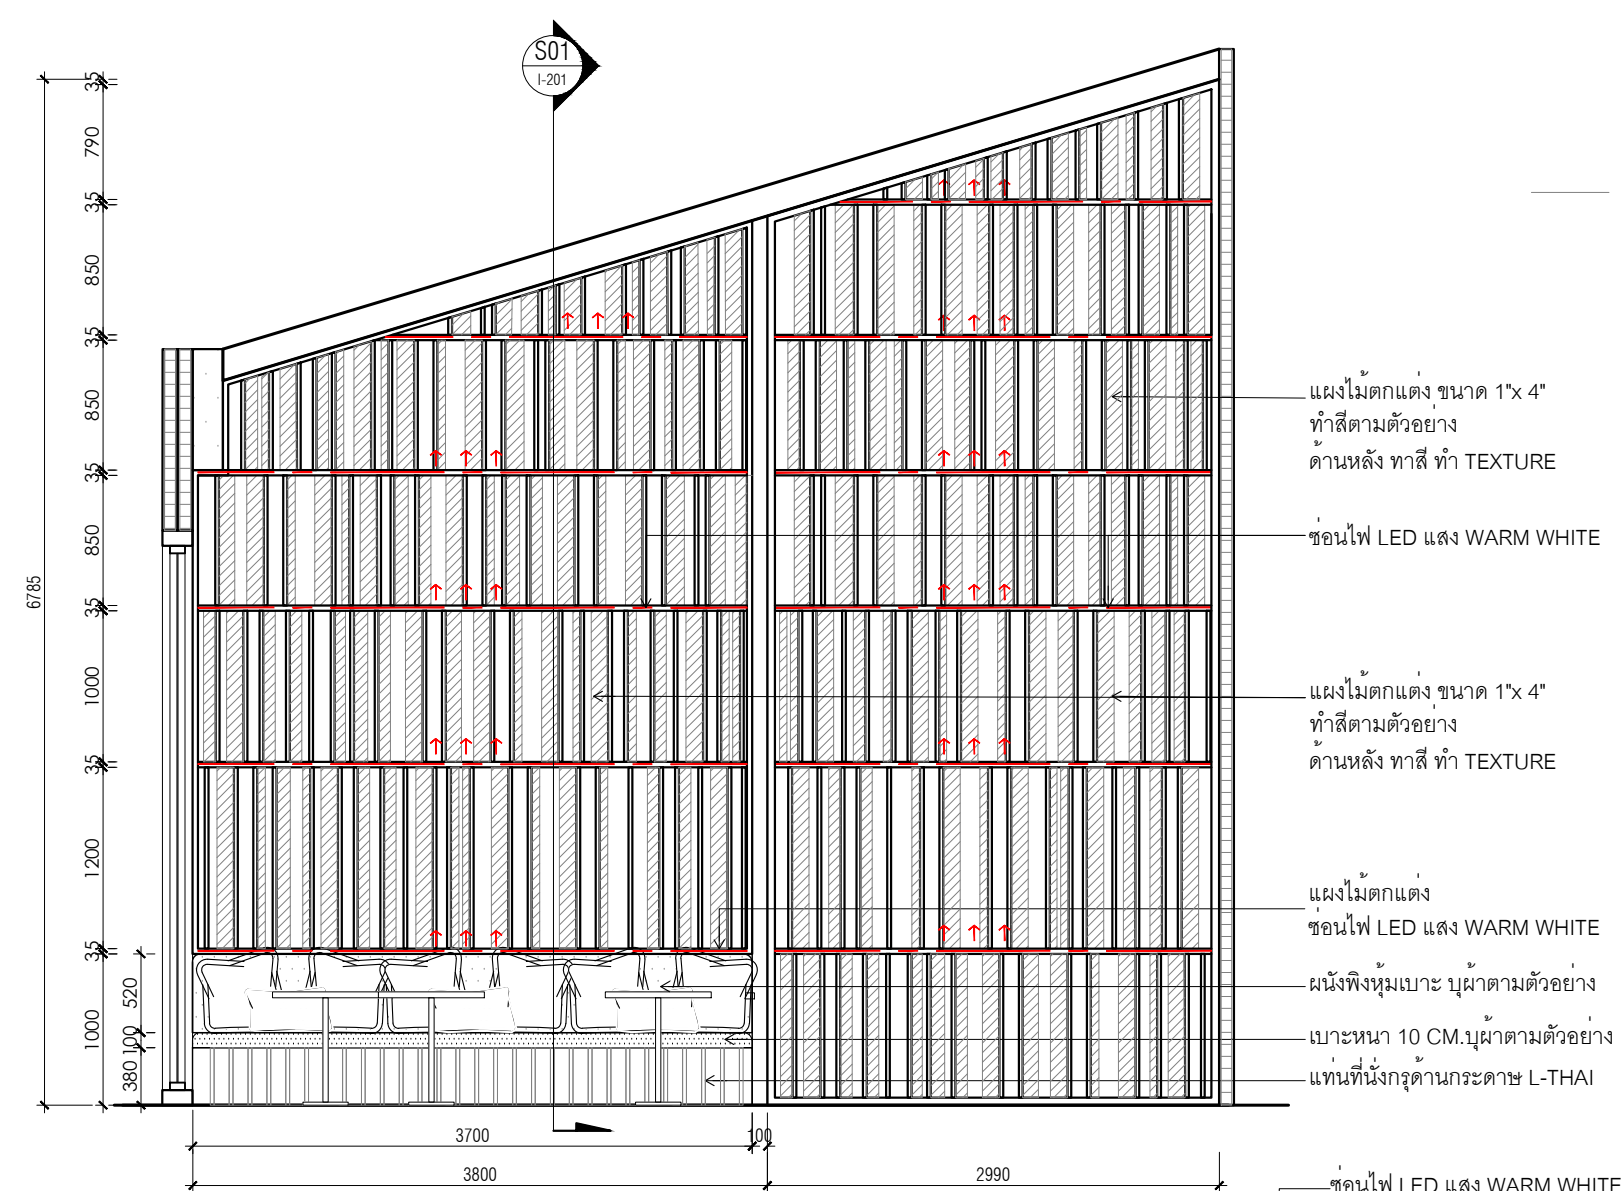


E01 ELEVATION 1 : 50
I-200 BAR - BANQUETTE SEATING

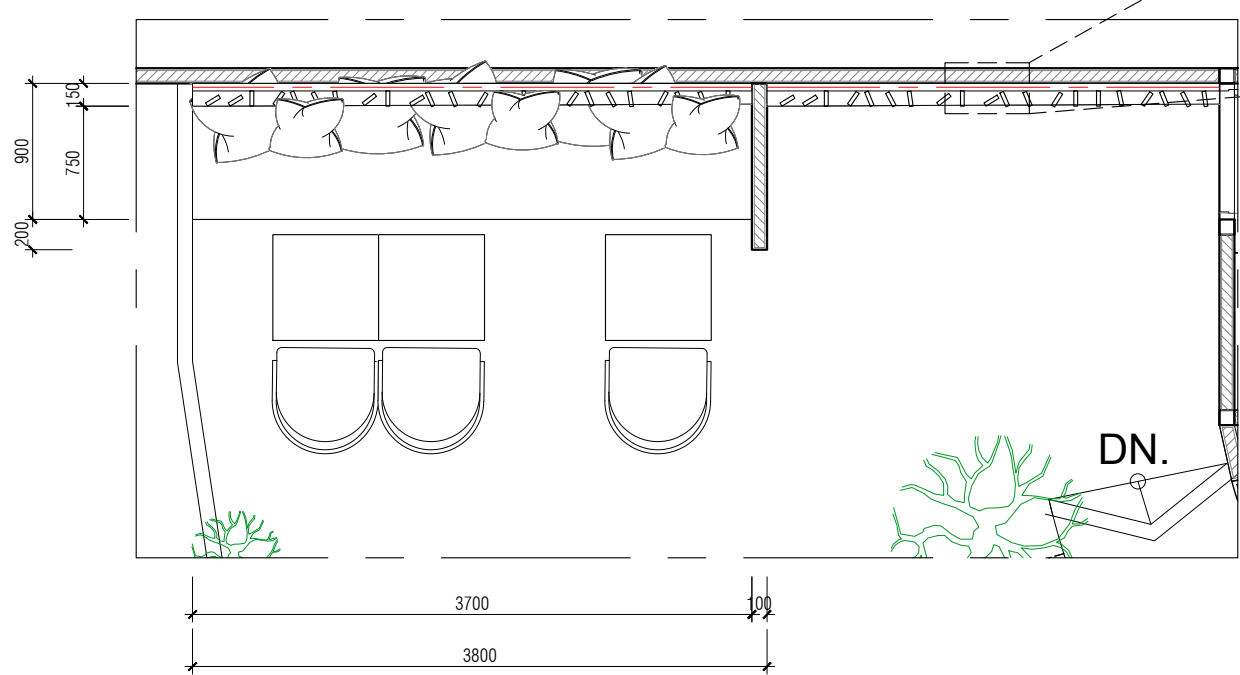


PLAN 1 : 50
BAR-BANQUETTE SEATING

- แผงไม้ตกแต่ง ขนาด 1"x 4" ทำสีตามตัวอย่าง ด้านหลัง ทาสี ทำ TEXTURE
- ซ่อนไฟ LED แสง WARM WHITE
- แผงไม้ตกแต่ง ขนาด 1"x 4" ทำสีตามตัวอย่าง ด้านหลัง ทาสี ทำ TEXTURE
- แผงไม้ตกแต่ง ซ่อนไฟ LED แสง WARM WHITE
- ผนังพองน้ำเบาะ บุผ้าตามตัวอย่าง
- เบาะหนา 10 CM.บุผ้าตามตัวอย่าง
- แท่นที่นั่งกรุด้านกระดาศ L-THAI
- ซ่อนไฟ LED แสง WARM WHITE
- แผงไม้ตกแต่ง ขนาด 1"x 4" ทำสีตามตัวอย่าง

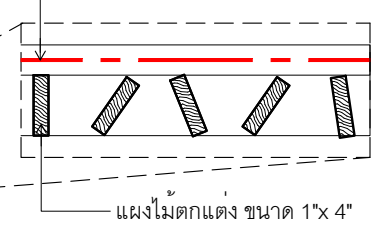


รูปภาพประกอบแบบผนังตกแต่ง

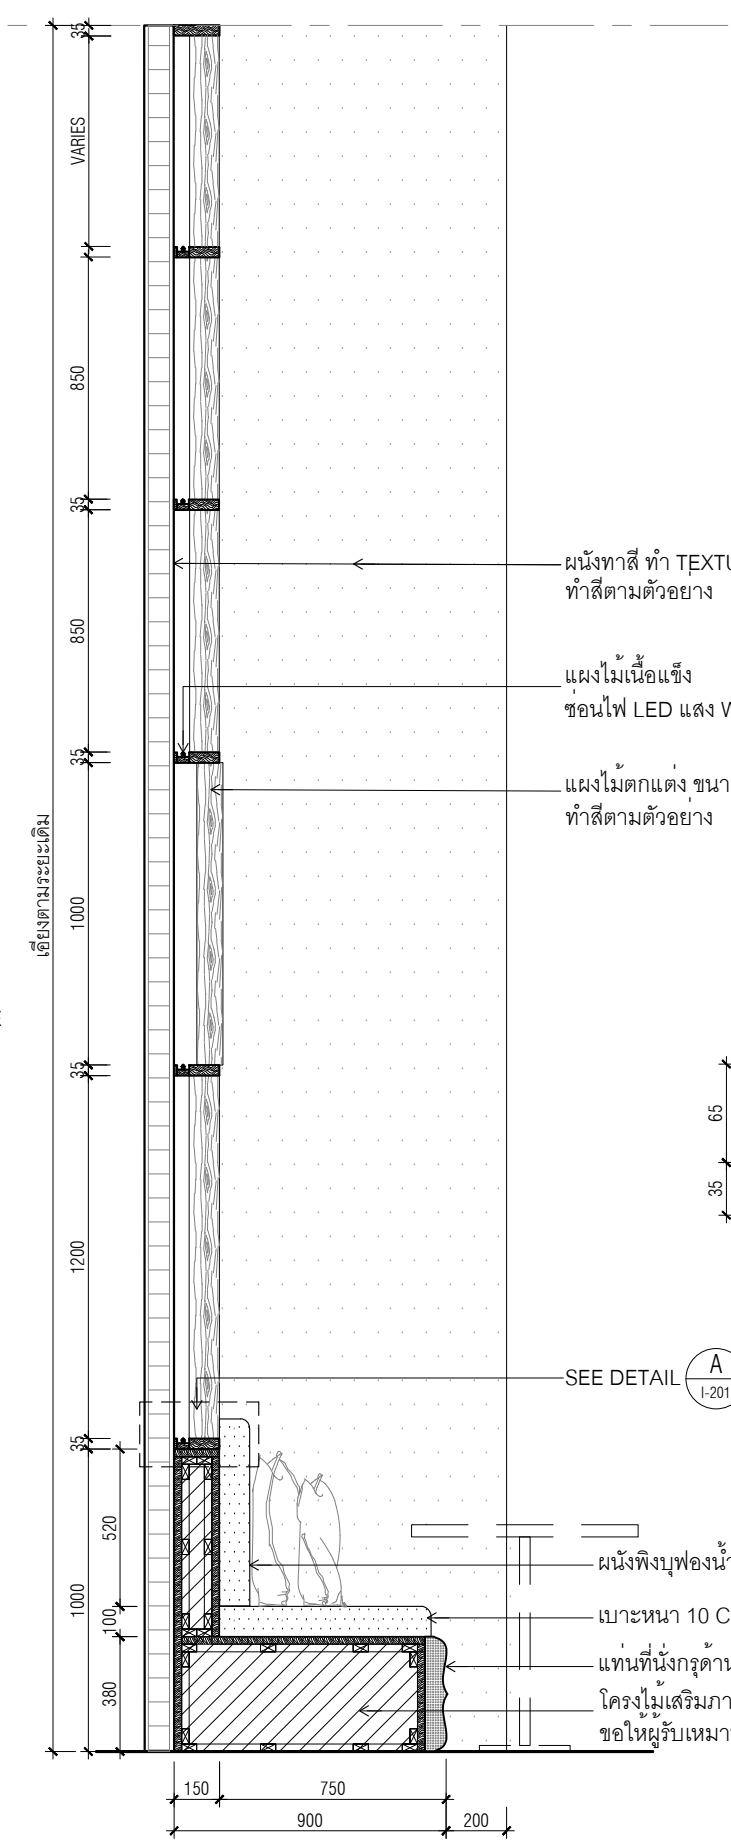

S01 SECTION 1 : 25
I-201 BAR - BANQUETTE SEATING


- ผนังทาสี ทำ TEXTURE ทำสีตามตัวอย่าง
- แผงไม้เนื้อแข็ง ซ่อนไฟ LED แสง WARM WHITE
- แผงไม้ตกแต่ง ขนาด 1"x 4" ทำสีตามตัวอย่าง

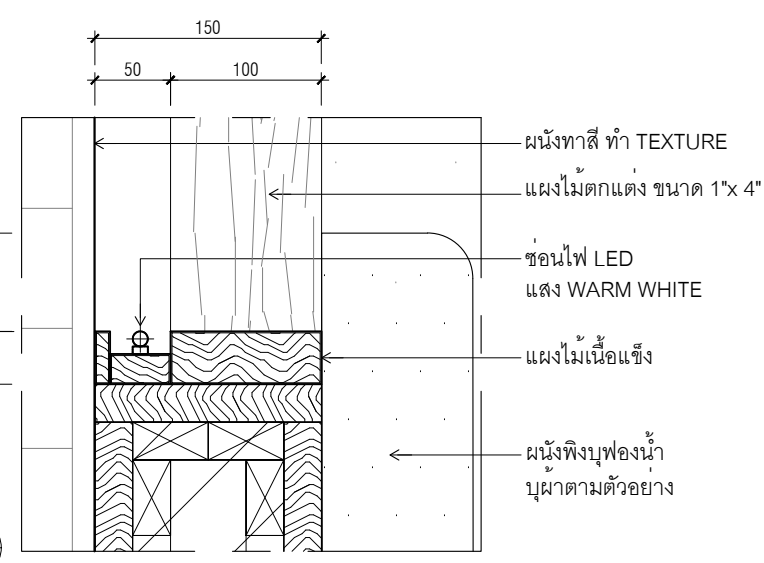

A DETAIL 1 : 5
I-201 BAR - BANQUETTE SEATING

- ผนังพองน้ำบุฟองน้ำ บุผ้าตามตัวอย่าง
- เบาะหนา 10 CM.บุผ้าตามตัวอย่าง
- แท่นที่นั่งกรุด้านกระดาศ L-THAI
- โครงไม้เสริมภายใน
- ขอให้ผู้รับเหมาหน้าเสนอ

- ผนังทาสี ทำ TEXTURE
- แผงไม้ตกแต่ง ขนาด 1"x 4"
- ซ่อนไฟ LED แสง WARM WHITE
- แผงไม้เนื้อแข็ง
- ผนังพองน้ำบุฟองน้ำ บุผ้าตามตัวอย่าง

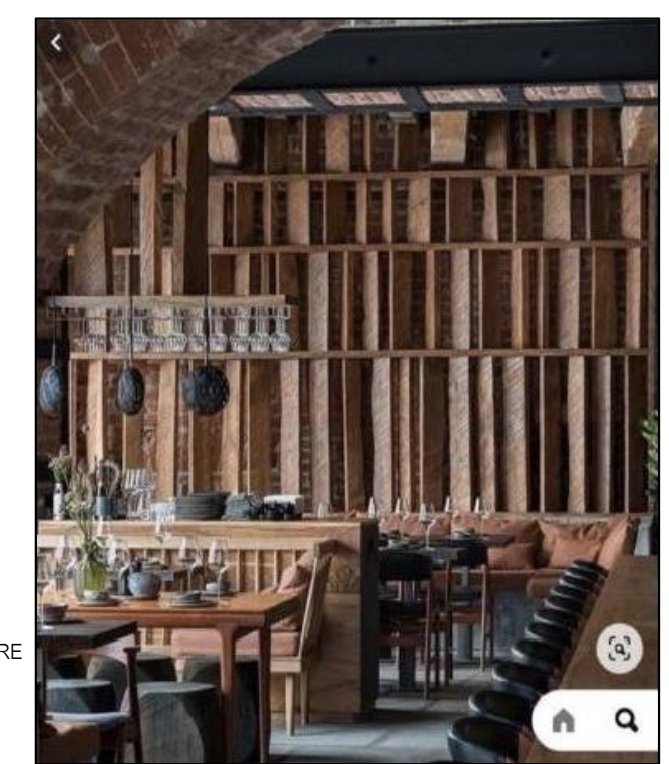

รูปภาพประกอบแบบผนังตกแต่ง




รูปภาพประกอบแบบผนังตกแต่ง

แผงตกแต่ง
กรูไมทอน ทำสีตามตัวอย่าง


ต้นไม้ตกแต่ง

SEE DETAIL A
I-202

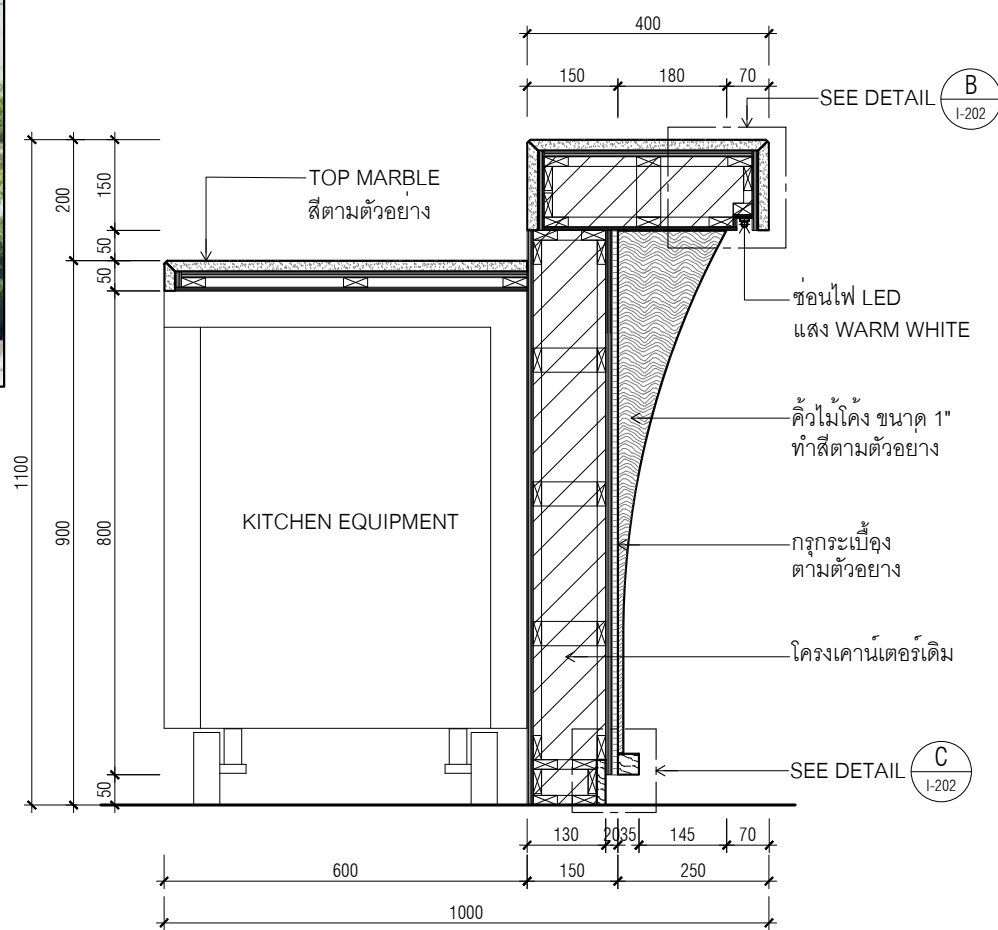


S01 SECTION 1 : 12.5

I-202 COUNTER BAR

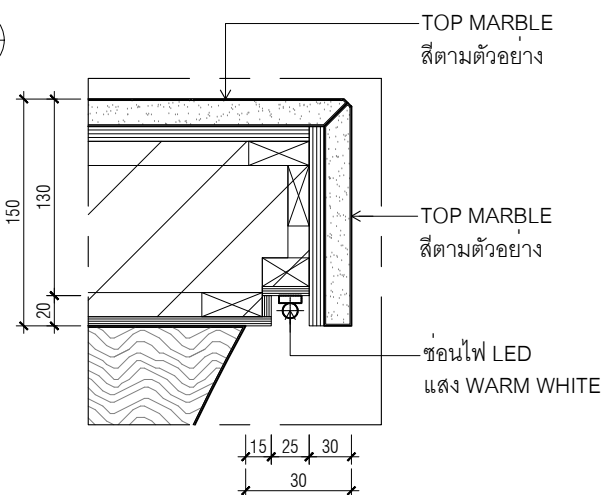



DETAIL B 1 : 5

I-202 COUNTER BAR

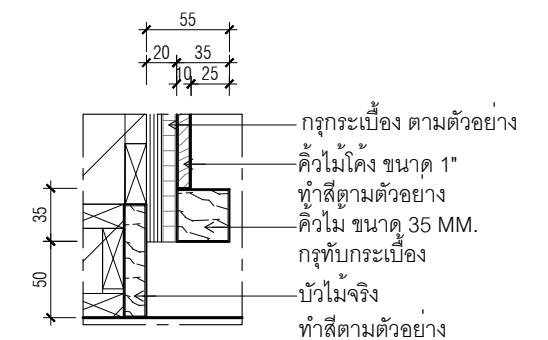

DETAIL C 1 : 5

I-202 COUNTER BAR

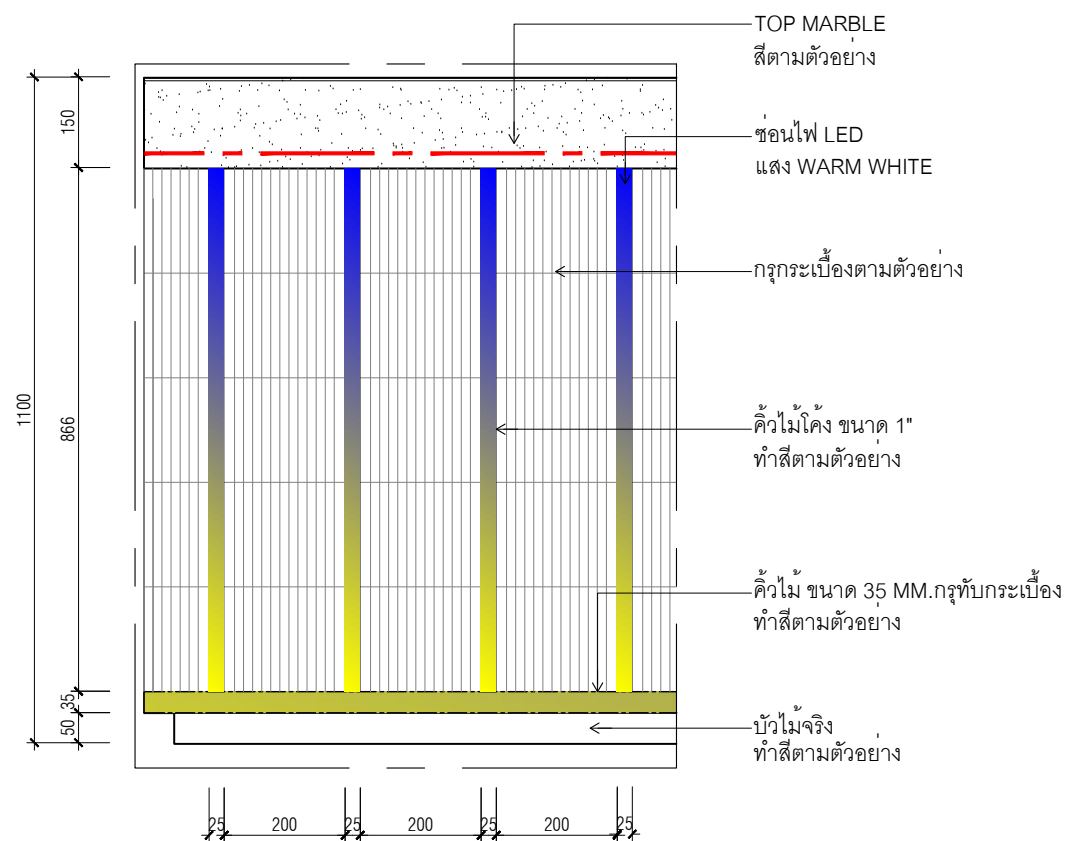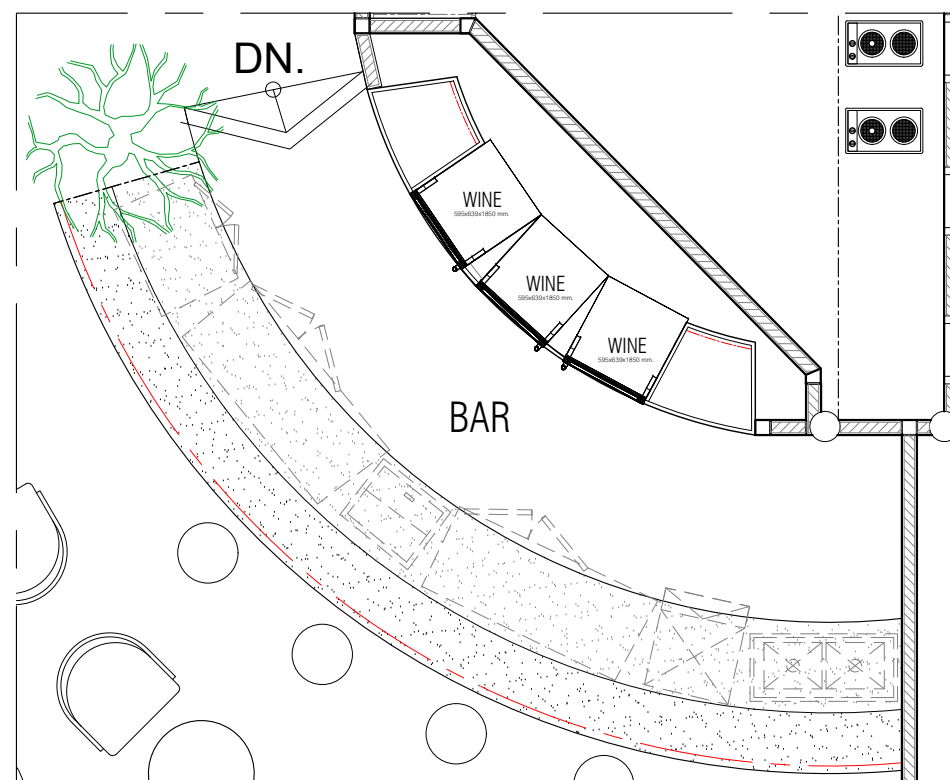


DETAIL A 1 : 12.5



I-202 COUNTER BAR




รูปภาพประกอบแบบเคาน์เตอร์


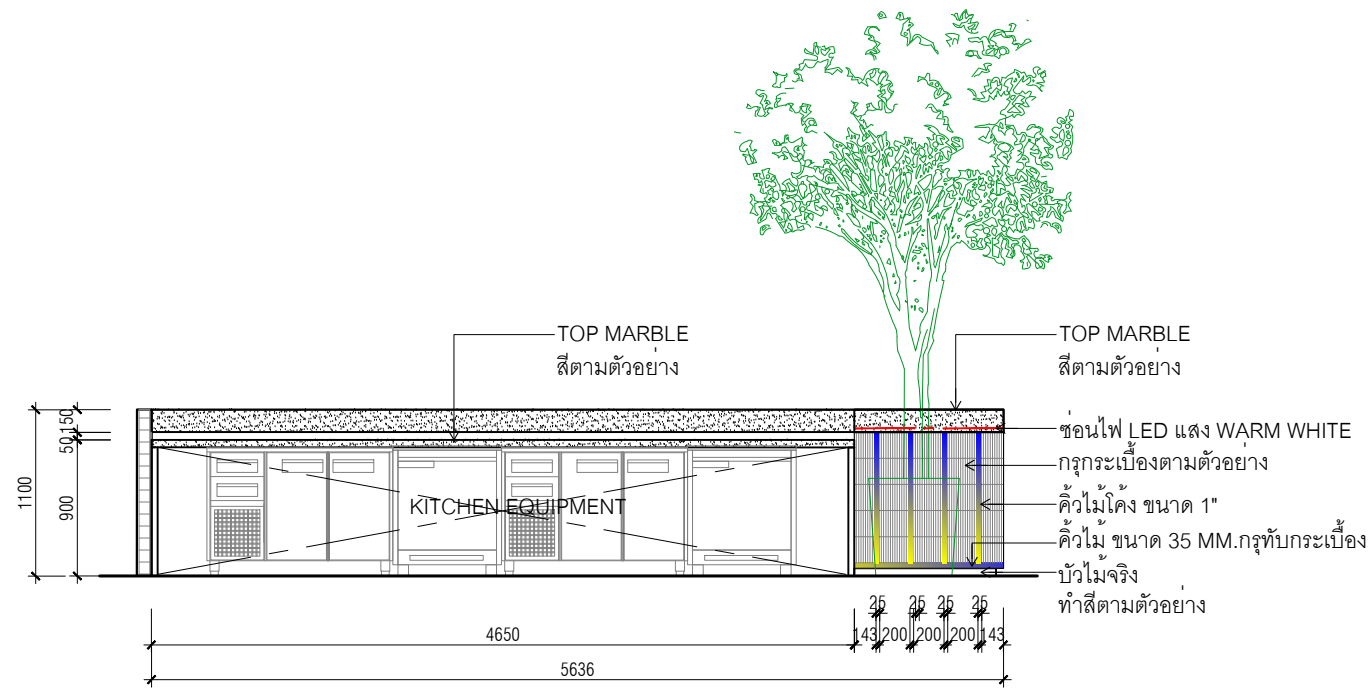



E03 ELEVATION 1 : 50
I-200 COUNTER BAR

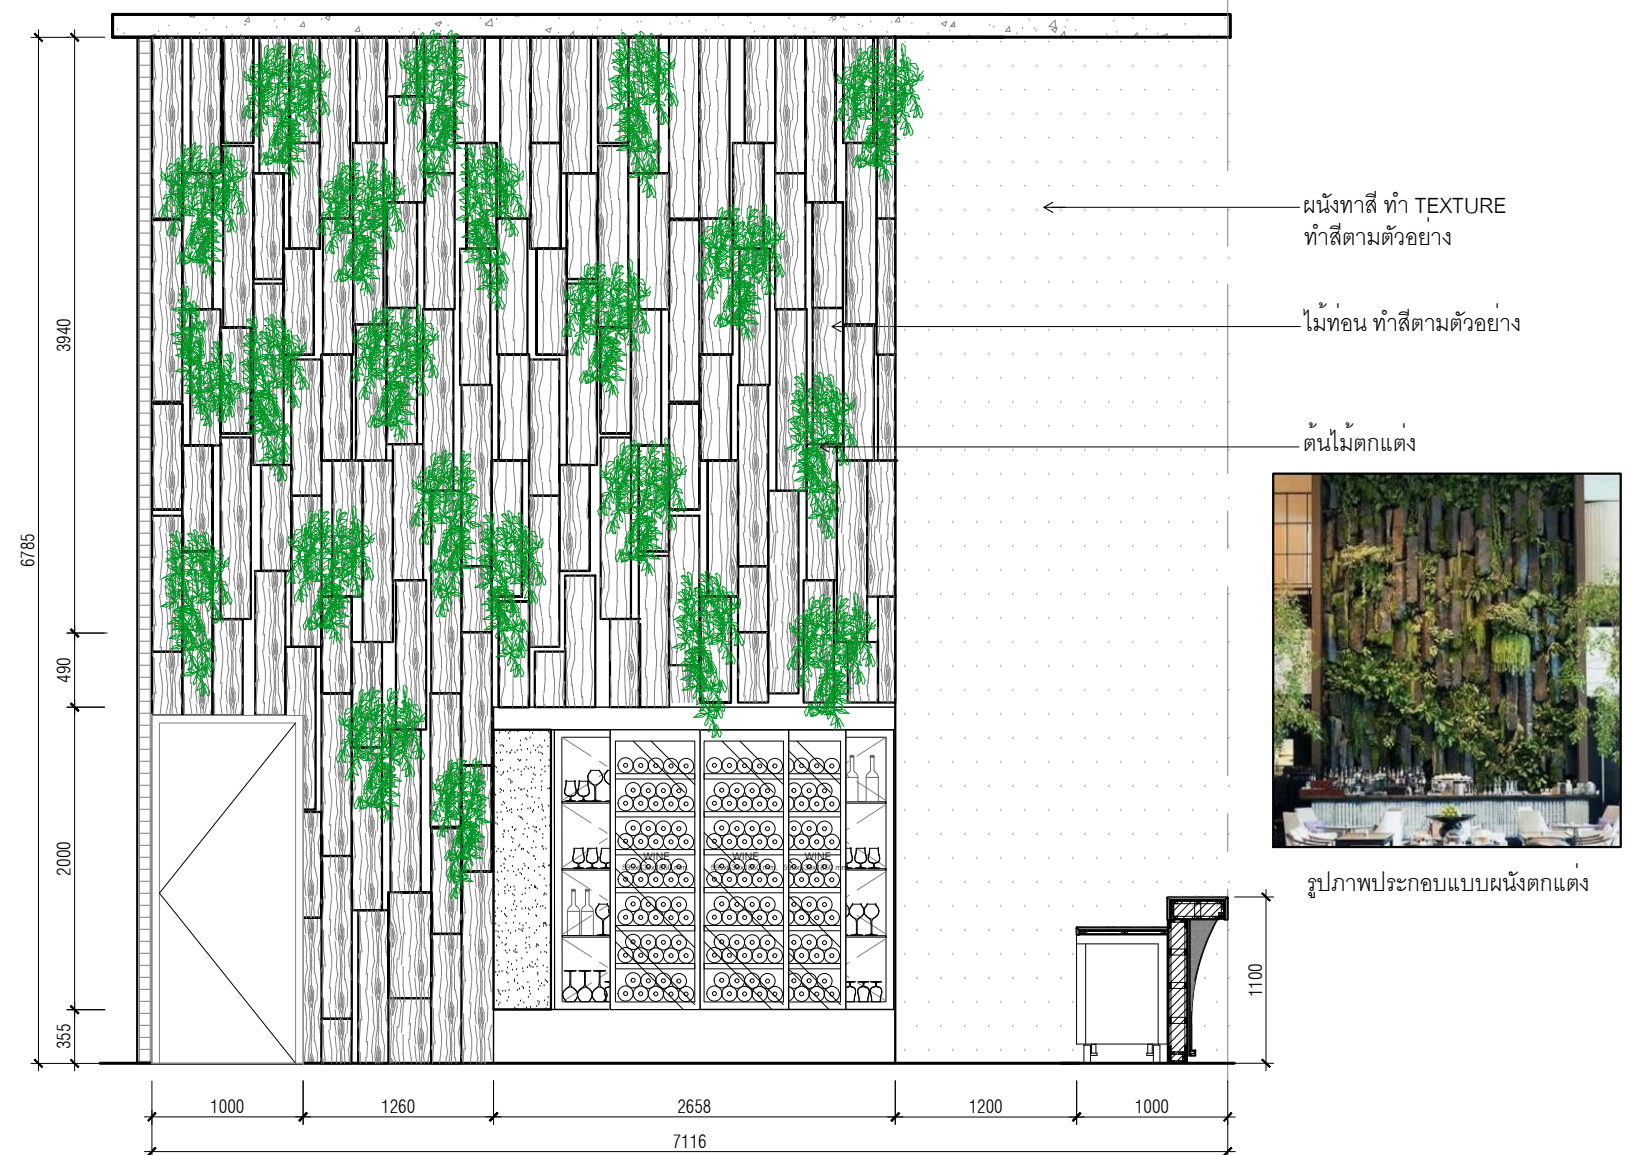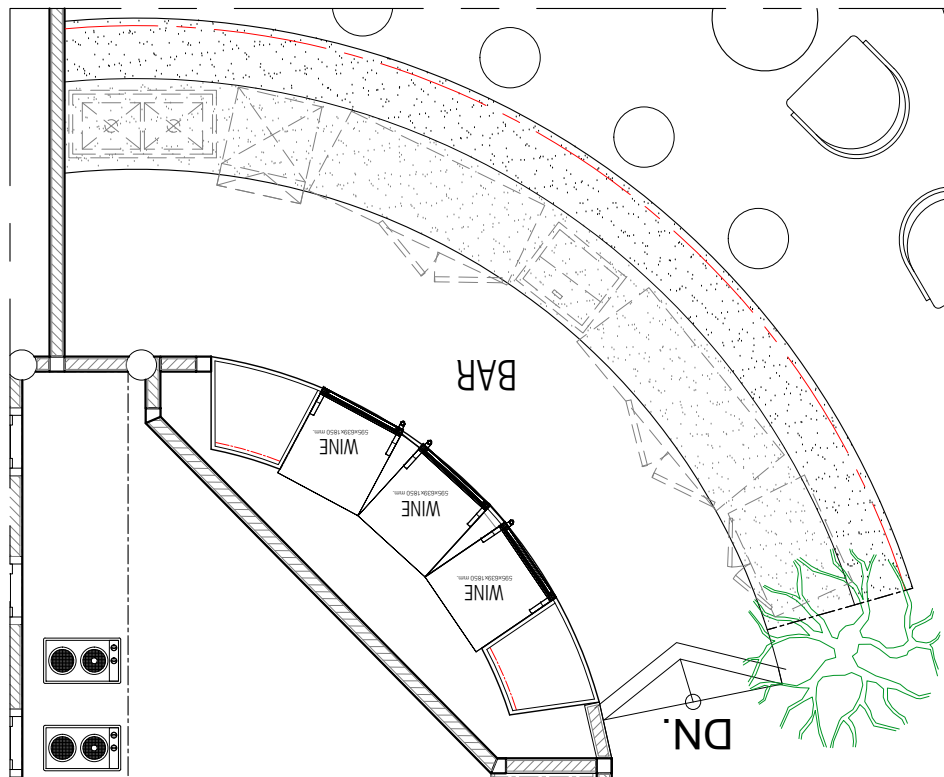


E04 ELEVATION 1 : 50
I-200 COUNTER BAR

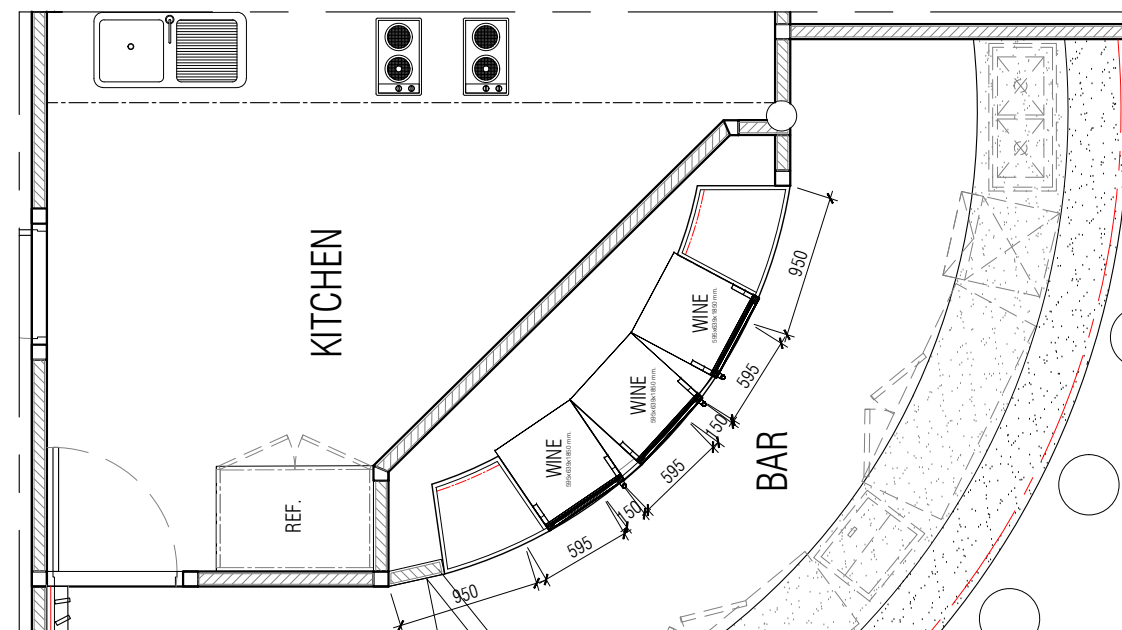

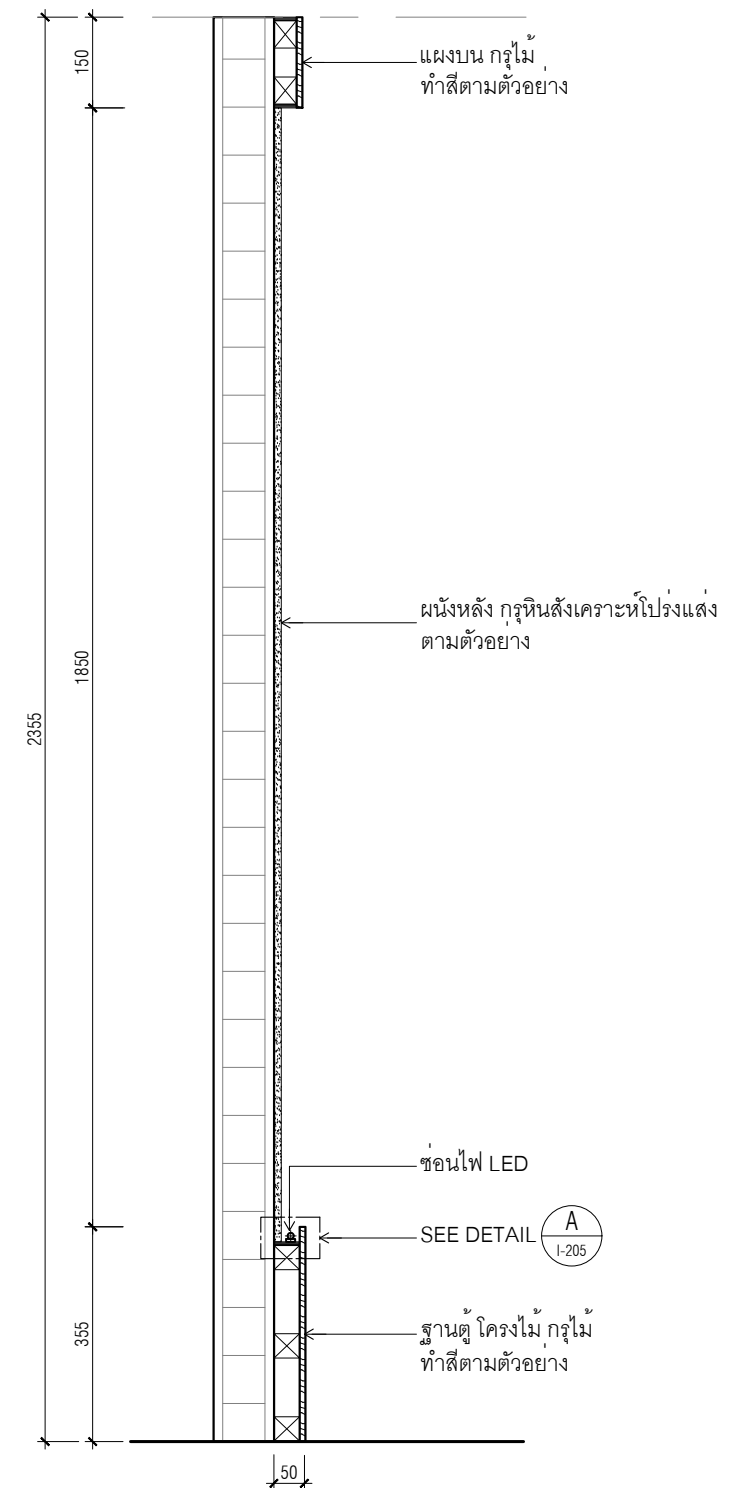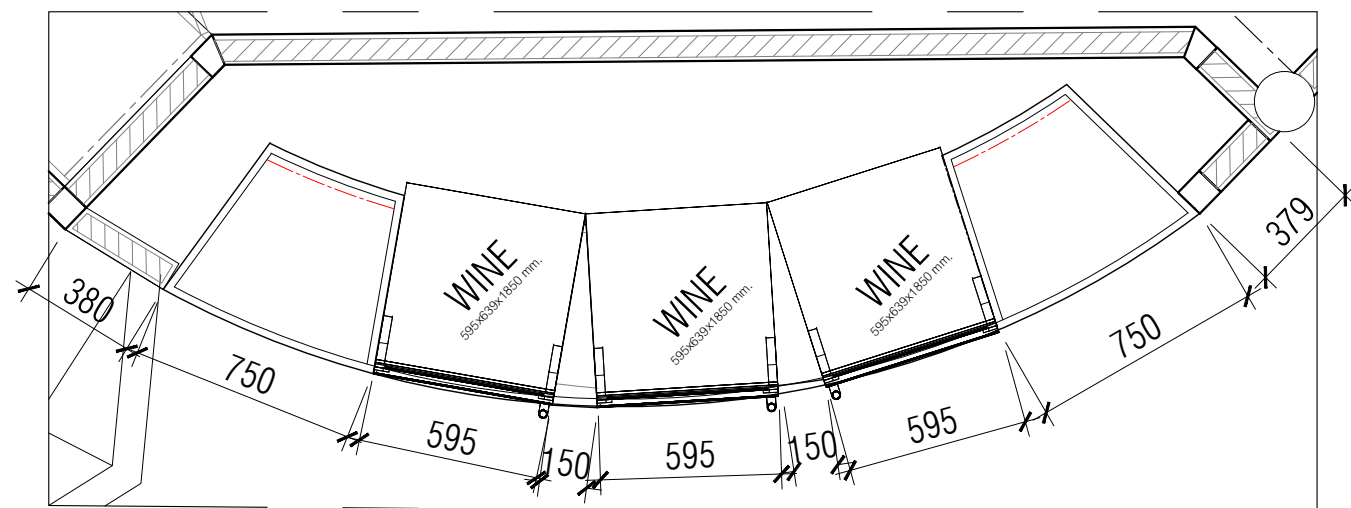


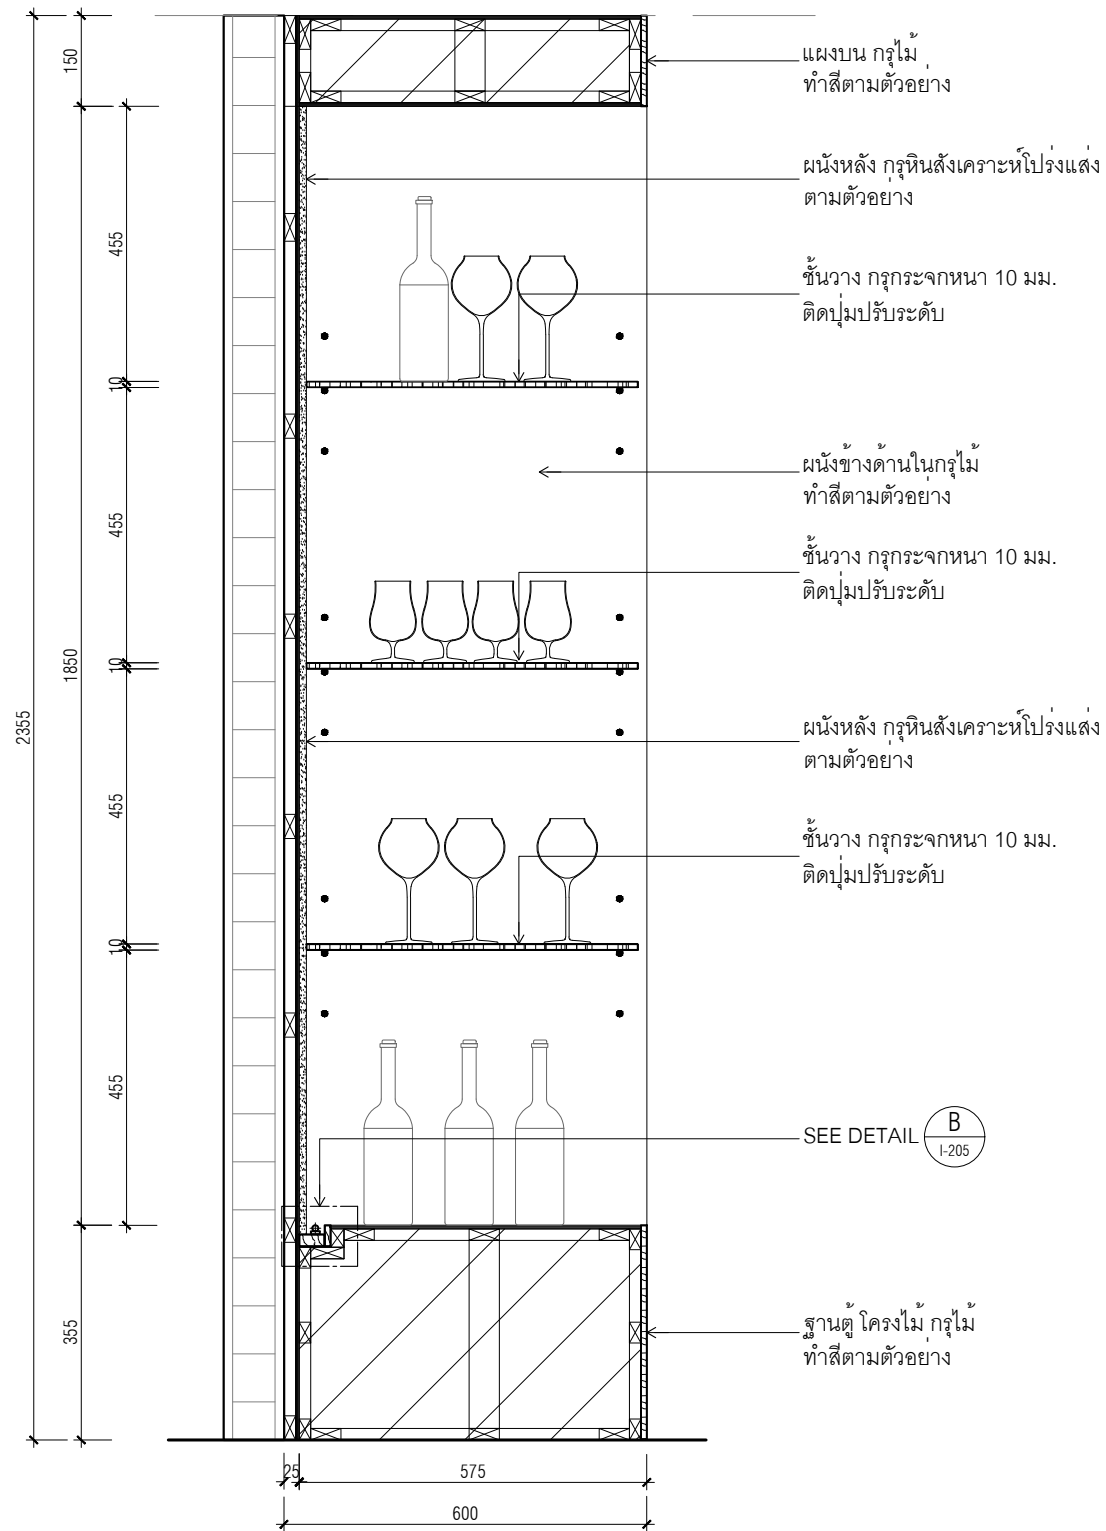


S02 SECTION 1 : 12.5
I-204 COUNTER BAR

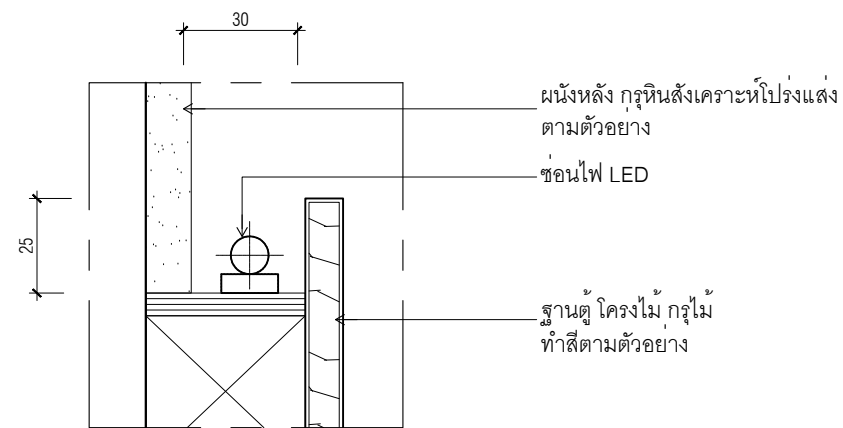

A DETAIL 1 : 2
I-204 COUNTER BAR

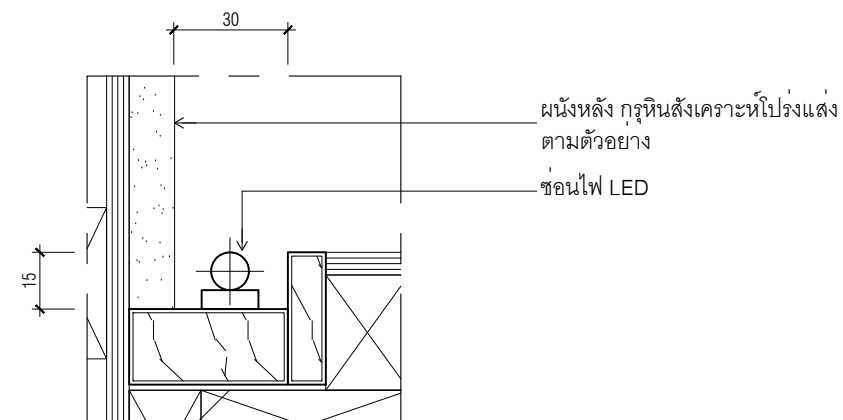

B DETAIL 1 : 2
I-204 COUNTER BAR

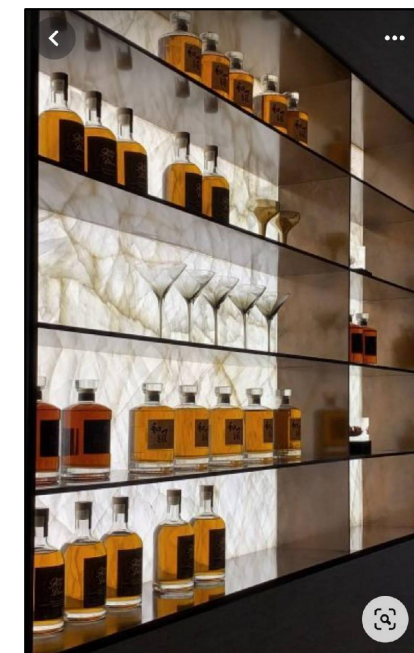

รูปภาพประกอบแบบชั้นวางแก้ว